



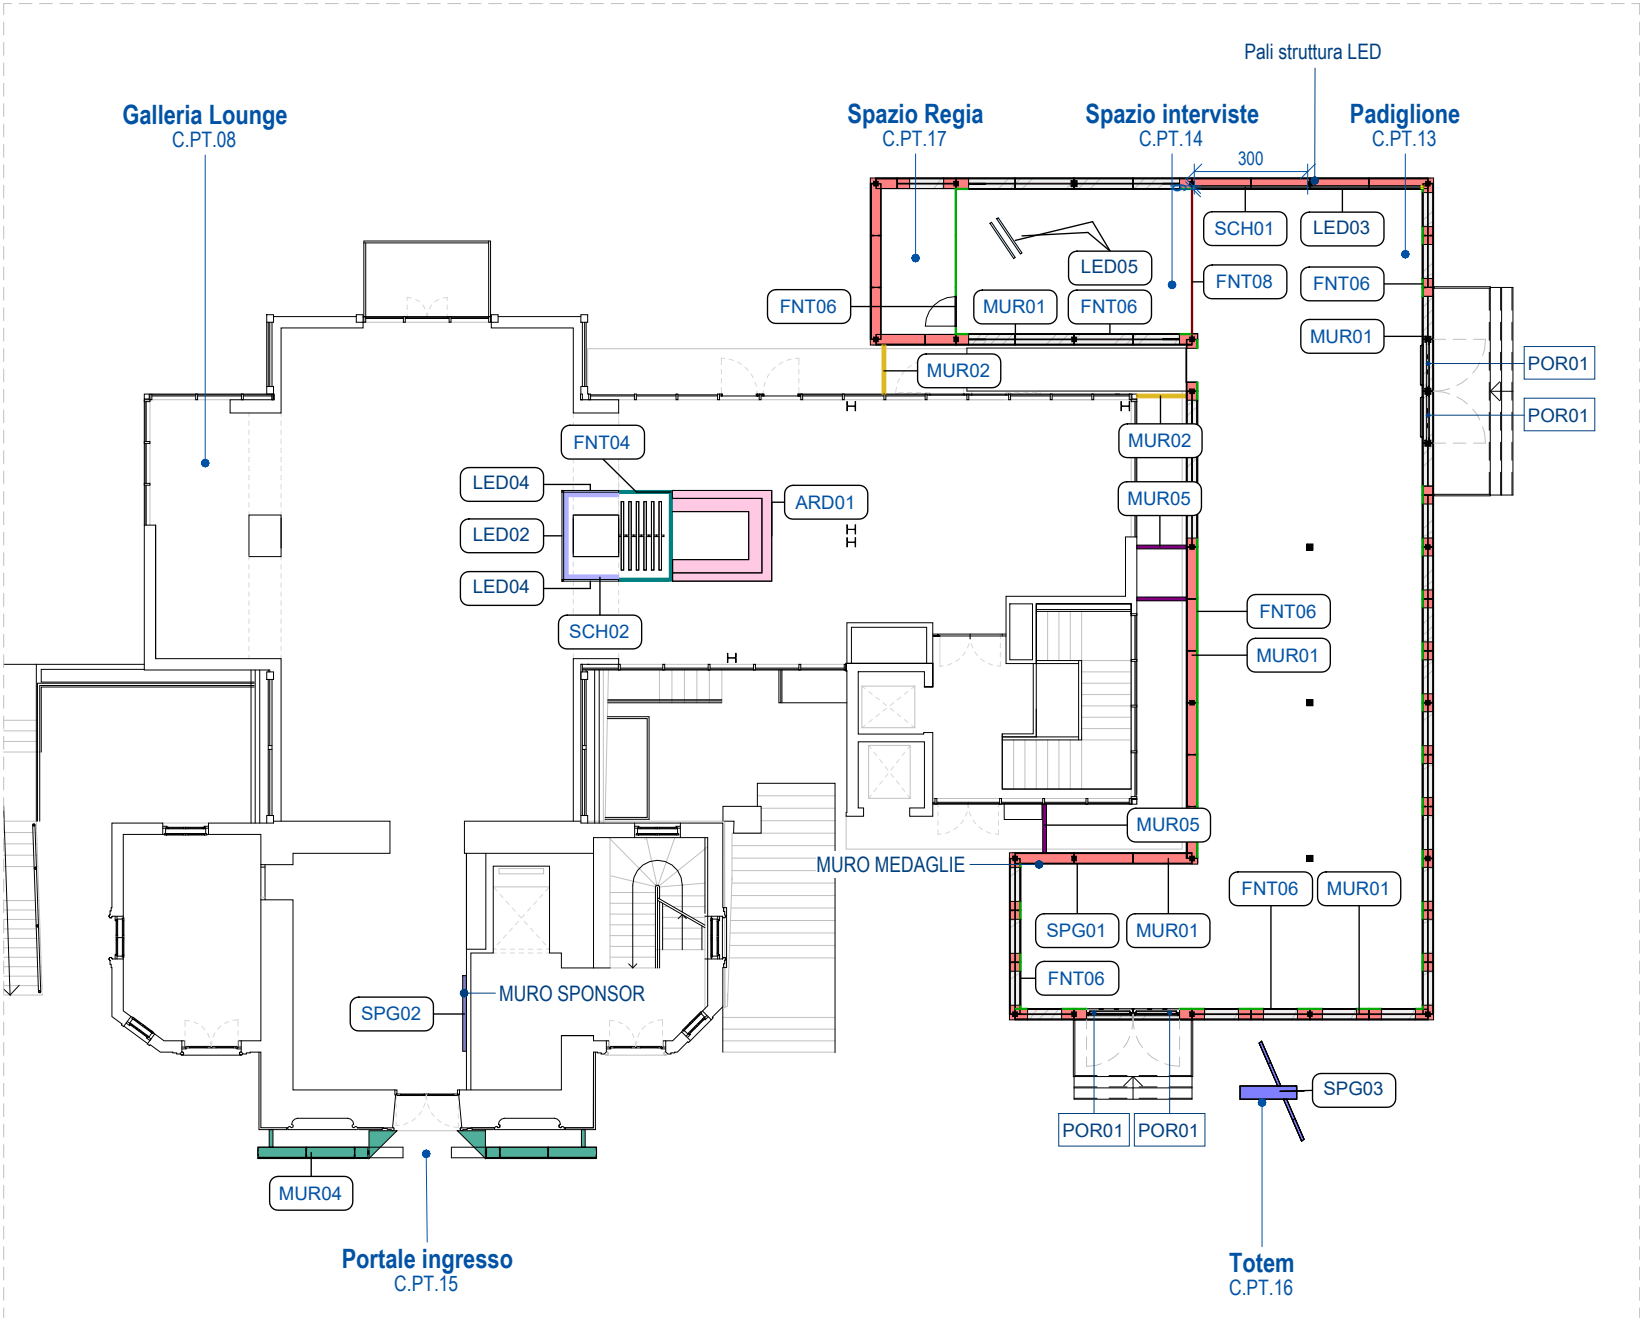

PIANTA PT - ABACO FINITURE VERTICALI
1 : 200

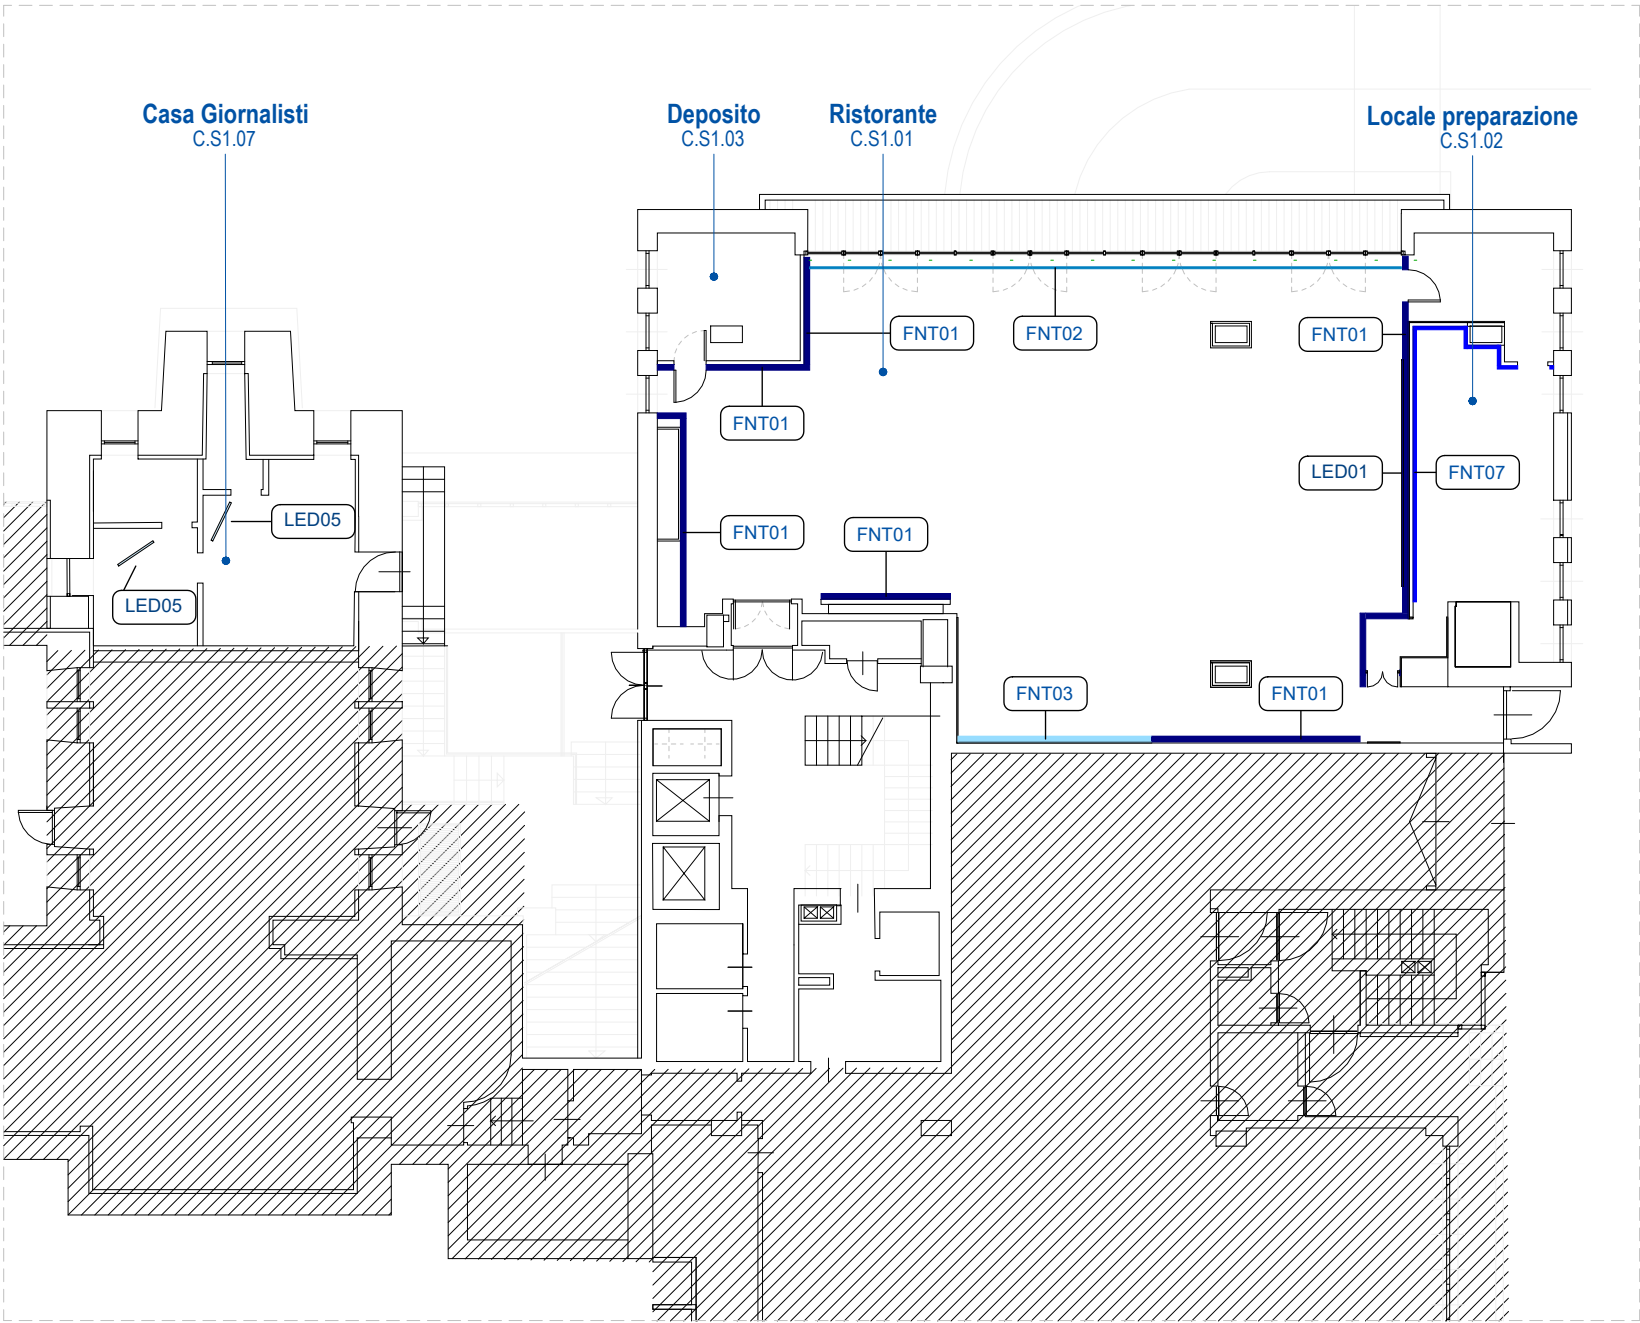

PIANTA PS1 - ABACO FINITURE VERTICALI
1 : 200

LEGENDA - ABACO - DISPOSITIVI AUDIO VIDEO

- LED01 Schermo LED dimensioni 600x250cm spessore 5mm
LED02 Schermo LED dimensioni 270x240cm spessore 4.5m con pannello MDF - Modulo 60x33.75cm
LED03 Schermo LED moduli 50x50cm dimensioni 250x600cm spessore 4.5mm
LED04 Schermo LED dimensioni 150x270cm spessore 4.5mm con pannello MDF 3cm - Modulo 60.33.75 con angolare 30x30
LED05 TV 55 Pollici Casa dei giornalisti / Spazio interviste

LEGENDA - ABACO - ELEMENTI VERTICALI

- FNT01 Parete in legno rivestita in essenza Ristorante
FNT02 Tende arricciate in tessuto Ristorante
FNT03 Parete in legno verniciata Ristorante
FNT04 Parete in legno con rivestimento metallico Galleria
FNT06 Parete in legno rivestita in essenza Padiglione e spazio interviste
FNT07 Parete isolante Locale preparazione
FNT08 Tenda arricciata in tessuto spazio interviste
MUR01 Parete esterna con rivestimento metallico e finestre e portefinestre in vetro Padiglione
MUR02 Parete esterna rivestimento metallico Padiglione
MUR04 Parete in legno per esterno con rivestimento metallico Portale ingresso
MUR05 Parete esterna in legno chiusura di servizio Padiglione
SCH01 Struttura di sostegno LED Padiglione
SCH02 Struttura di sostegno LED Galleria
SPG01 Parete spazio grafica - Muro delle medaglie
SPG02 Parete spazio grafica - Muro degli sponsor
SPG03 Totem Casa Italia
POR 01 Porta a vetri con maniglione antipanico

LEGENDA - ABACO - ARREDI SU MISURA

- ARD01 Bancone aperitivo finitura metallica

NOTE GENERALI:

- Tutte le misure indicate devono essere verificate in sito prima della realizzazione.
- In caso di discrepanze tra gli elaborati progettuali, prevalgono quelli architettonici redatti in scala maggiore e con livello di dettaglio superiore.
- Nel presente elaborato, il posizionamento di dispositivi quali schermi e monitor (identificati con i codici LED-NumeroProgressivo è fornito a titolo indicativo, ai fini del coordinamento architettonico. La fornitura e la posa dei dispositivi suddetti non sono comprese nell'appalto.
- L'ingombro e il posizionamento delle opere d'arte sono riportati come indicazione generale e devono essere verificati in sito. La fornitura delle opere non è inclusa nell'appalto.
- Le indicazioni relative al posizionamento degli apparecchi illuminanti presenti in questo elaborato hanno valore puramente orientativo. Per la progettazione e realizzazione dell'impianto di illuminazione fare riferimento agli elaborati specifici. Tutte le installazioni dovranno essere conformi ai requisiti normativi vigenti.
- Le indicazioni relative alla posizione dei dispositivi antincendio esistenti sono da considerarsi indicative. Posizione, quantità e ingombro dovranno essere verificati in sito. Salvo diversa indicazione, non è consentito modificare, ostruire o intervenire sugli impianti esistenti in modo da comprometterne la funzionalità.
- Nel presente elaborato la posizione e ingombro degli arredi è fornito come pura indicazione ai fini del coordinamento architettonico degli elementi. Salvo diversa indicazione gli arredi sono da considerarsi esclusi dal presente appalto.

ALLESTIMENTO CASA ITALIA "MUSA" - Olimpiadi invernali Milano Cortina 2026

Farsettiarte Cortina
Piazza Roma, 10, 32043 Cortina d'Ampezzo BL



COMMITTENTE:



CONI
Comitato Olimpico Nazionale
Piazza Lauro de Bosis, 15
Roma (RM)

COORDINAMENTO:



IT'S
Via Ignazio Pettinengo, 72
00159 - Roma (RM)

PROGETTAZIONE ARCHITETTONICA: it's IT'S Arch. Paolo Mezzalama Via Ignazio Pettinengo, 72 00159 - Roma (RM)	PROGETTAZIONE ARREDI: Atelier BE PG Atelier BEPG Agence: 11 rue Pierre Picard 75018 Paris Siège social: 1 avenue Christian Doppler 77700 Serris	GRAFICA: NERO NERO Lungotevere degli Artigiani 8/b 00153 Rome Italy	CURATELA ARTISTICA: EXELETRO FONICA Ex Electrofonica Vicolo Sant'Onofrio, 10 00165 Rome (IT)	PROGETTAZIONE ILLUMINOTECNICA: FABER Fabertecnica Via C. B. Vaccolini 14 00153 Rome (IT)
PROGETTAZIONE IMPIANTI: Studio Leopizzi Studio Leopizzi Via Vincenzo Ussani, 90 00151 Roma (RM)	PROGETTAZIONE ANTINCENDIO: EMINENCE EMINENCE CONSULTING Palazzo Doria Pangnelli Via del Plebiscolto n. 112 - 00186 Roma	PROGETTAZIONE ILLUMINAZIONE ESTERNA: MASSIMO PASCUCCI PROJECT MASSIMO PASCUCCI PROJECT Via dei Vellari, 22 00121 Roma		

NOME PROGETTO:

148 Casa Italia "Musa" - Cortina

FASE PROGETTUALE:

PROGETTO ESECUTIVO

PROGETTISTA:

IT'S

TITOLO DOCUMENTO:

PIANTE - ABACO FV

DATA:

08/08/2025

SCALA:

1:200

FIRMA:

00	08/08/2025	ITS		Prima emissione
REV	DATA	DIS	CONT	DESCRIZIONE

CODICE PROGETTO	LIVELLO PROGETTO	DISCIPLINA	NUMERO ELABORATO	TIPO ELABORATO	NOME ELABORATO	REVISIONE
148C	PE	ARC	401	ABA	FV	00