



CORTINA 1.2

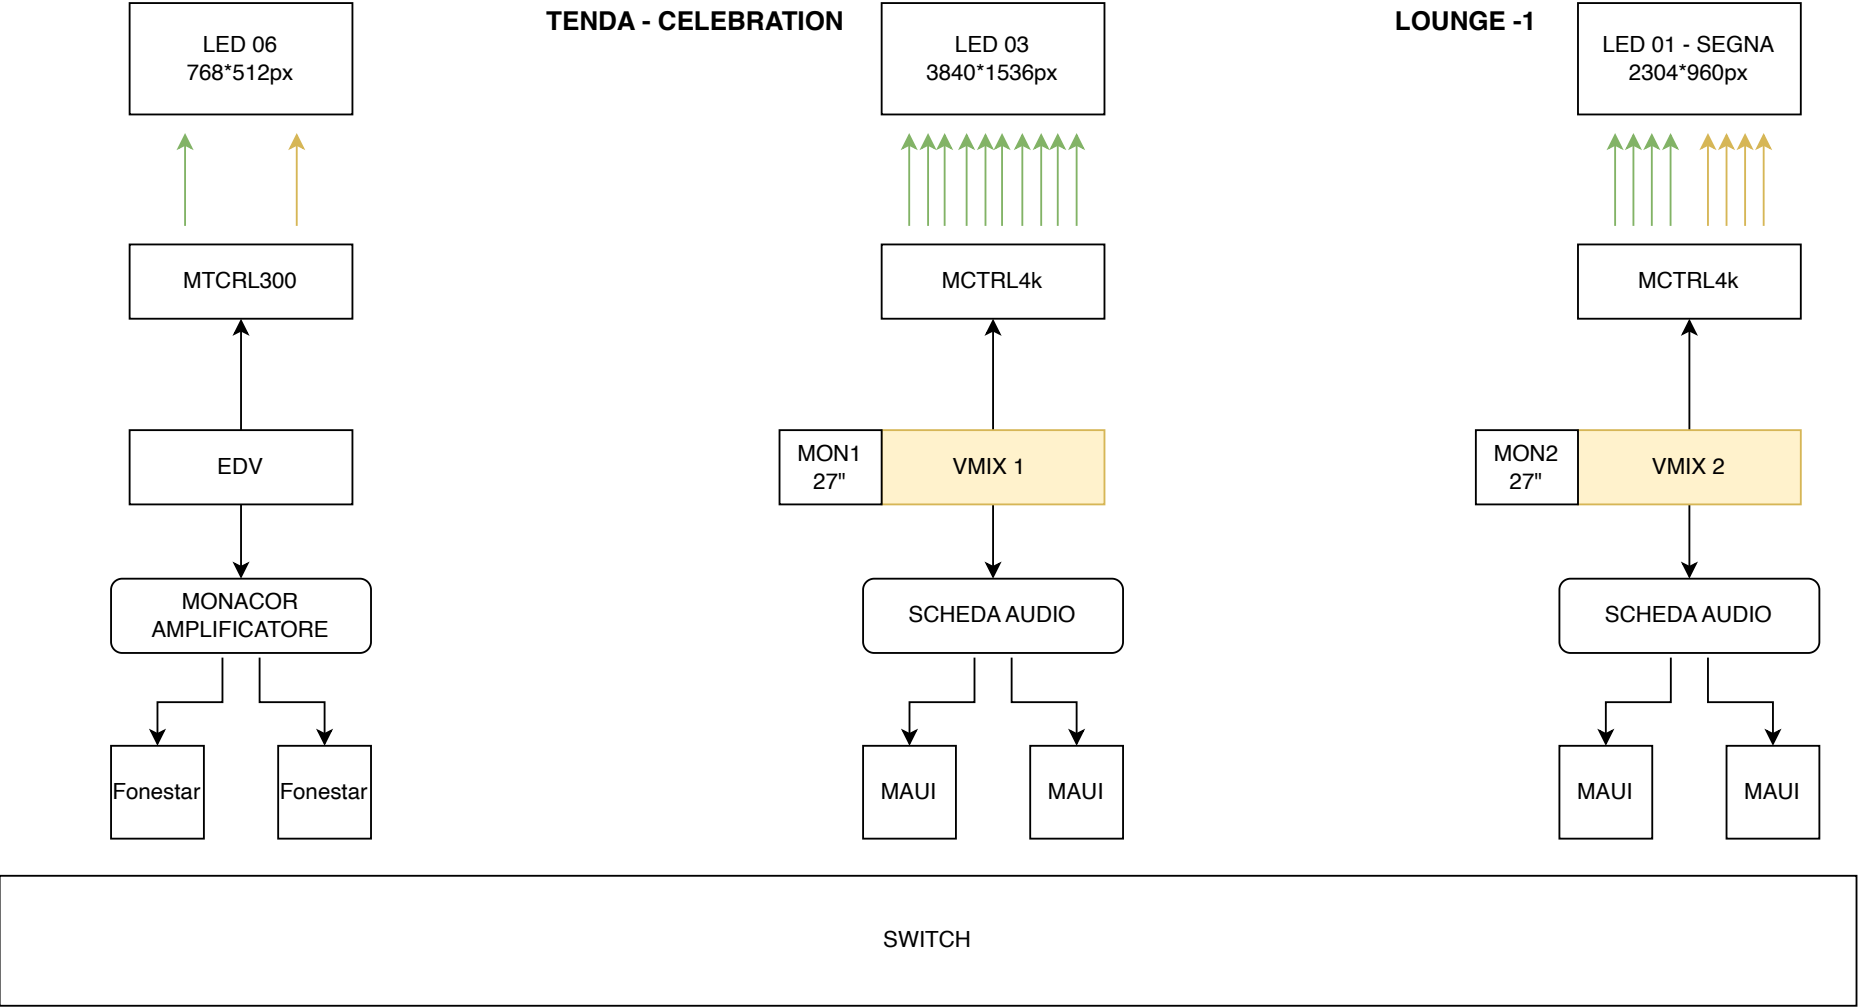

GALLERIA

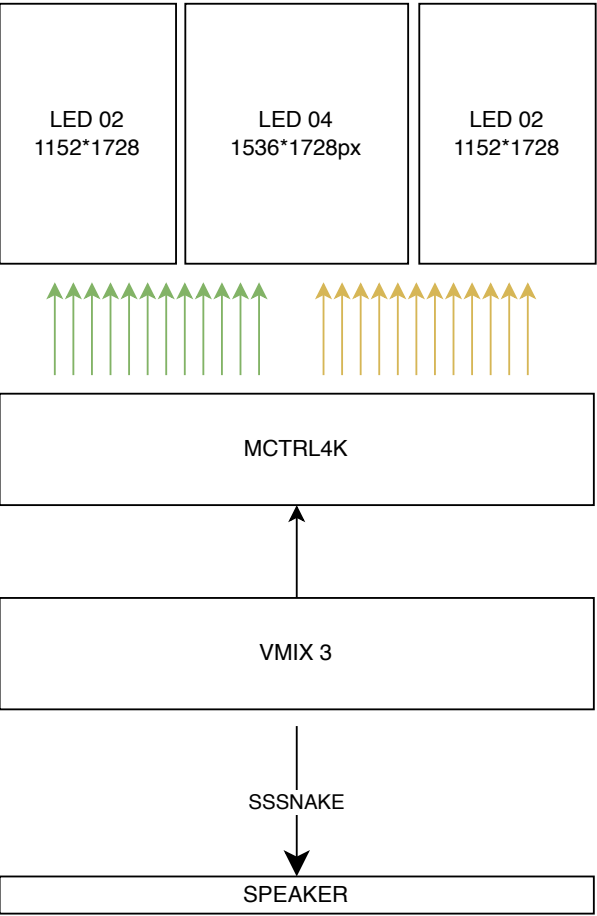

SCHEMA REGIA

